
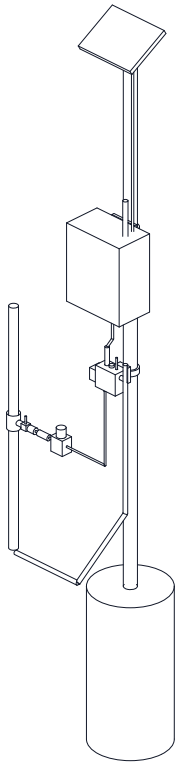


CONCEPT, NOT FOR FABRICATION

WaterWatch · github.com/BoujeeEnjinia1701/waterwatch

REV	DESCRIPTION	DATE	BY
P1	Preliminary GA for TRL 3 (from cad/src/model.py)	2026-09-25	AC
P2	Plugged pH probe port in cell lid (DDR-002)	2026-09-25	AC

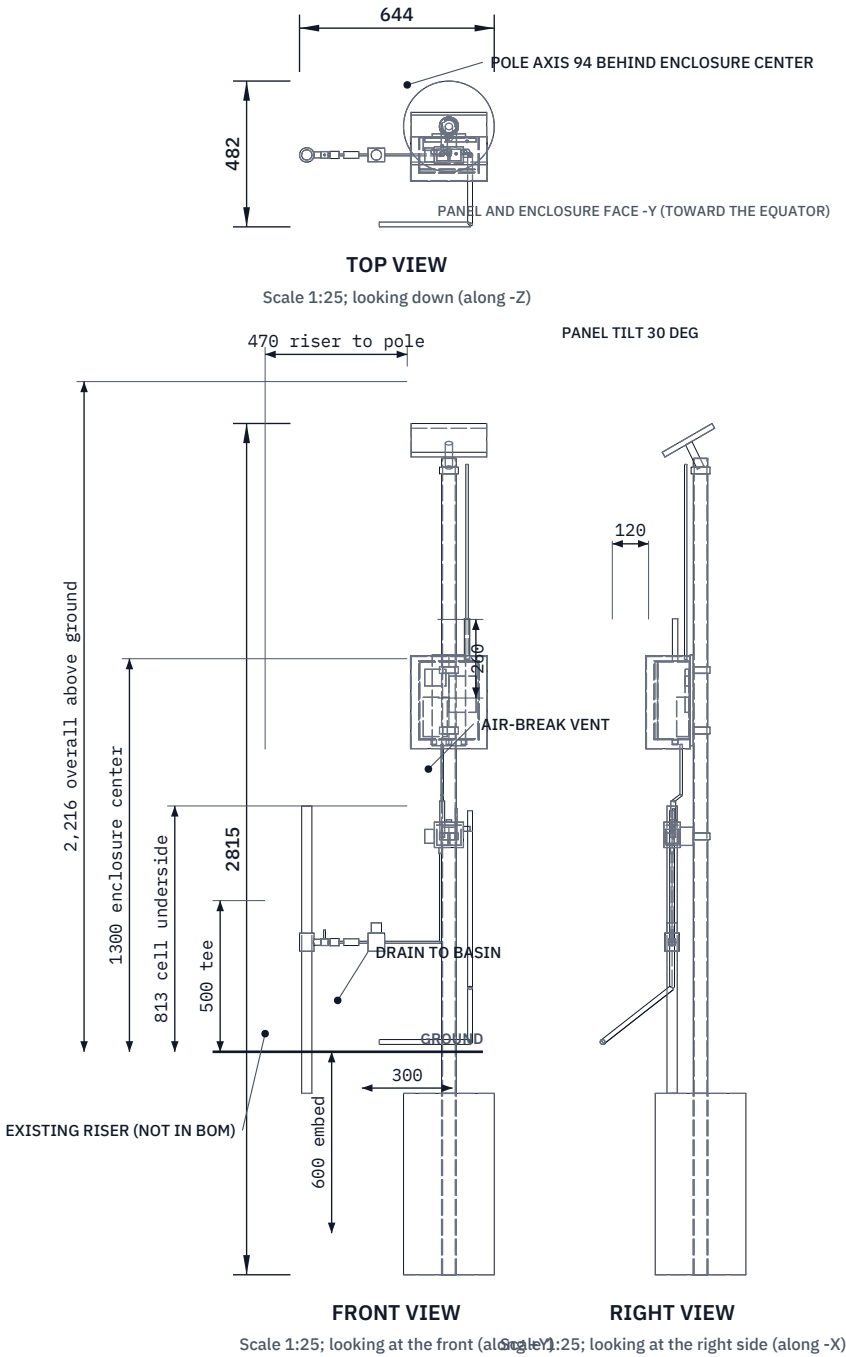

ISOMETRIC VIEW

Not to scale; seen from the front right and above, about 30 deg elevation

MAIN DIMENSIONS AND INTERFACES (MM)

- Pole 48.3 x 3.2 galvanized, 2100 above ground, 600 in a 300 footing
- Panel 5 W, 250 x 190, tilt 30 deg; top 2,216 above ground
- Enclosure IP66 200 x 120 x 260, center 1300; sun shield, 25 gap
- Flow cell body 96 x 54 x 74 + 10 lid; cavity 80 x 38 x 66
- Cell water 0.19 L; inlet at the bottom, outlet 62 above the underside
- Spare 12 pH probe port in cell lid, plugged (DDR-002)
- Tee on the 25 mm riser at 500; 1/4 in tube, 738 run, 11 mL
- Flush 0.5 L/min (pressure compensating) for 90 s hourly (WWT-CAL-001)
- Drain 12 mm bore with open air break; discharges to the basin
- Third-angle; front view from -Y; riser on the Z axis

WATERWATCH				github.com/BoujeeEnjinia1701/waterwatch			
General arrangement							
DRAWING NO. WWT-DWG-001			REV P2		SHEET 1 of 1		SIZE ANSI B
SCALE 1:25	UNITS mm	PROJECTION 		DATE 2026-09-25		DRAWN Amish Chadha	
MATERIAL / NOTES Galvanized steel pole; bought-in parts per bom/bom.csv. PRELIMINARY, NOT FOR FABRICATION							
Licensed CERN-OHL-S-2.0 · Design Molecule Lab · designmolecule.com						Generated from cad/src; do not edit by hand	