
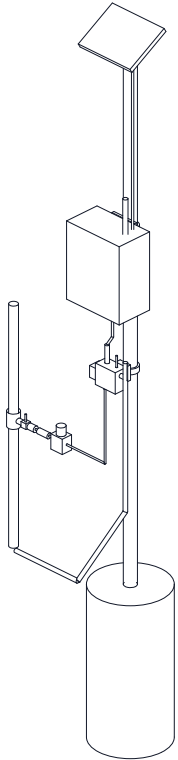


CONCEPT, NOT FOR FABRICATION

REV	DESCRIPTION	DATE	BY
P1	Preliminary GA for TRL 3 (from cad/src/model.py)	2026-09-25	AC

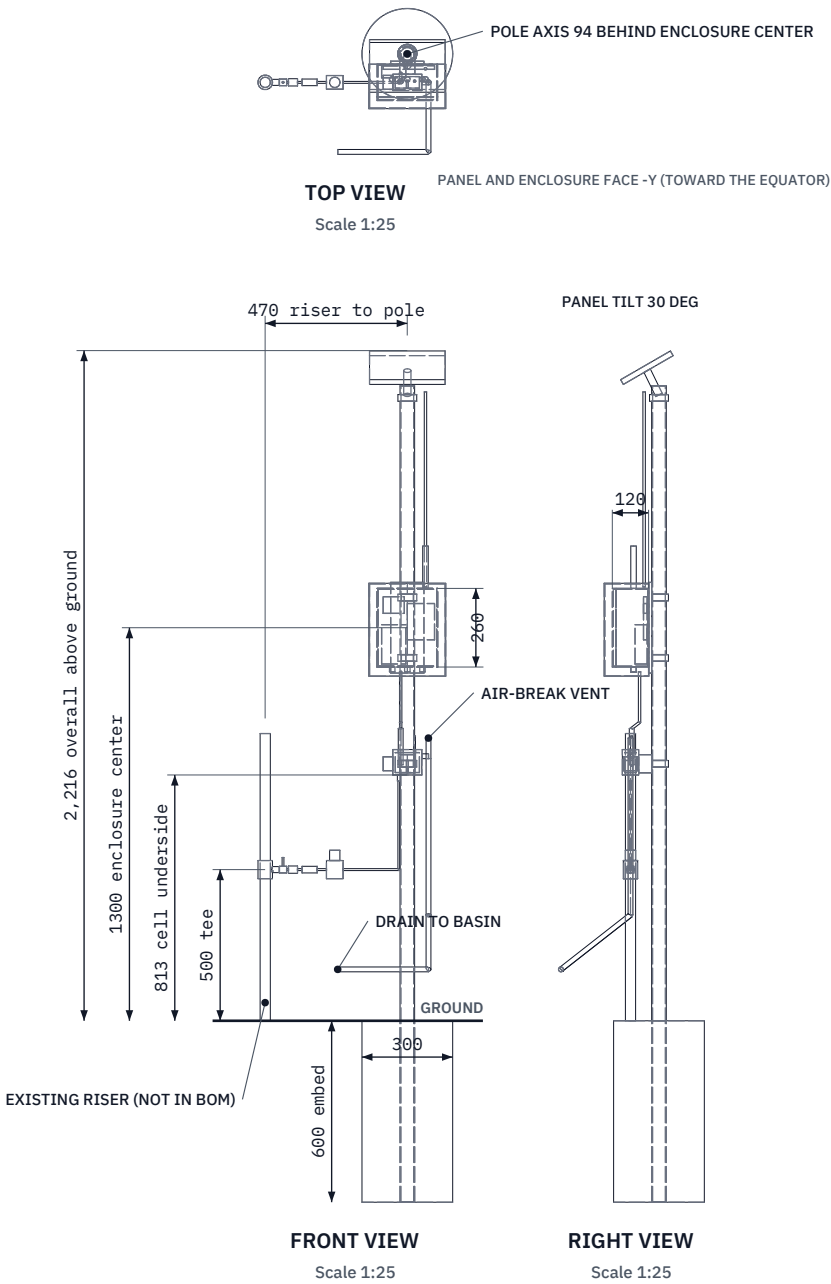

ISOMETRIC VIEW
Not to scale

MAIN DIMENSIONS AND INTERFACES (MM)

Pole 48.3 x 3.2 galvanized, 2100 above ground, 600 in a 300 footing

Panel 5 W, 250 x 190, tilt 30 deg; top 2,216 above ground

Enclosure IP66 200 x 120 x 260, center 1300; sun shield, 25 gap

Flow cell body 96 x 54 x 74 + 10 lid; cavity 80 x 38 x 66

Cell water 0.19 L; inlet at the bottom, outlet 62 above the underside

Tee on the 25 mm riser at 500; 1/4 in tube, 738 run, 11 mL

Flush 0.5 L/min (pressure compensating) for 90 s hourly (WWT-CAL-001)

Drain 12 mm bore with open air break; discharges to the basin

Third-angle; front view from -Y; riser on the Z axis

WATERWATCH

General arrangement

DRAWING NO. WWT-DWG-001		REV P1	SHEET 1 of 1	SIZE ANSI B
SCALE 1:25	UNITS mm	PROJECTION 	DATE 2026-09-25	DRAWN Amish Chadha
MATERIAL / NOTES Galvanized steel pole; bought-in parts per bom/bom.csv. PRELIMINARY, NOT FOR FABRICATION				
Licensed CERN-OHL-S-2.0 · Open Hardware Portfolio · amishchadha.com			Generated from cad/src; do not edit by hand	