


CONCEPT, NOT FOR FABRICATION

WaterWatch · github.com/BoujeeEnjinia1701/waterwatch

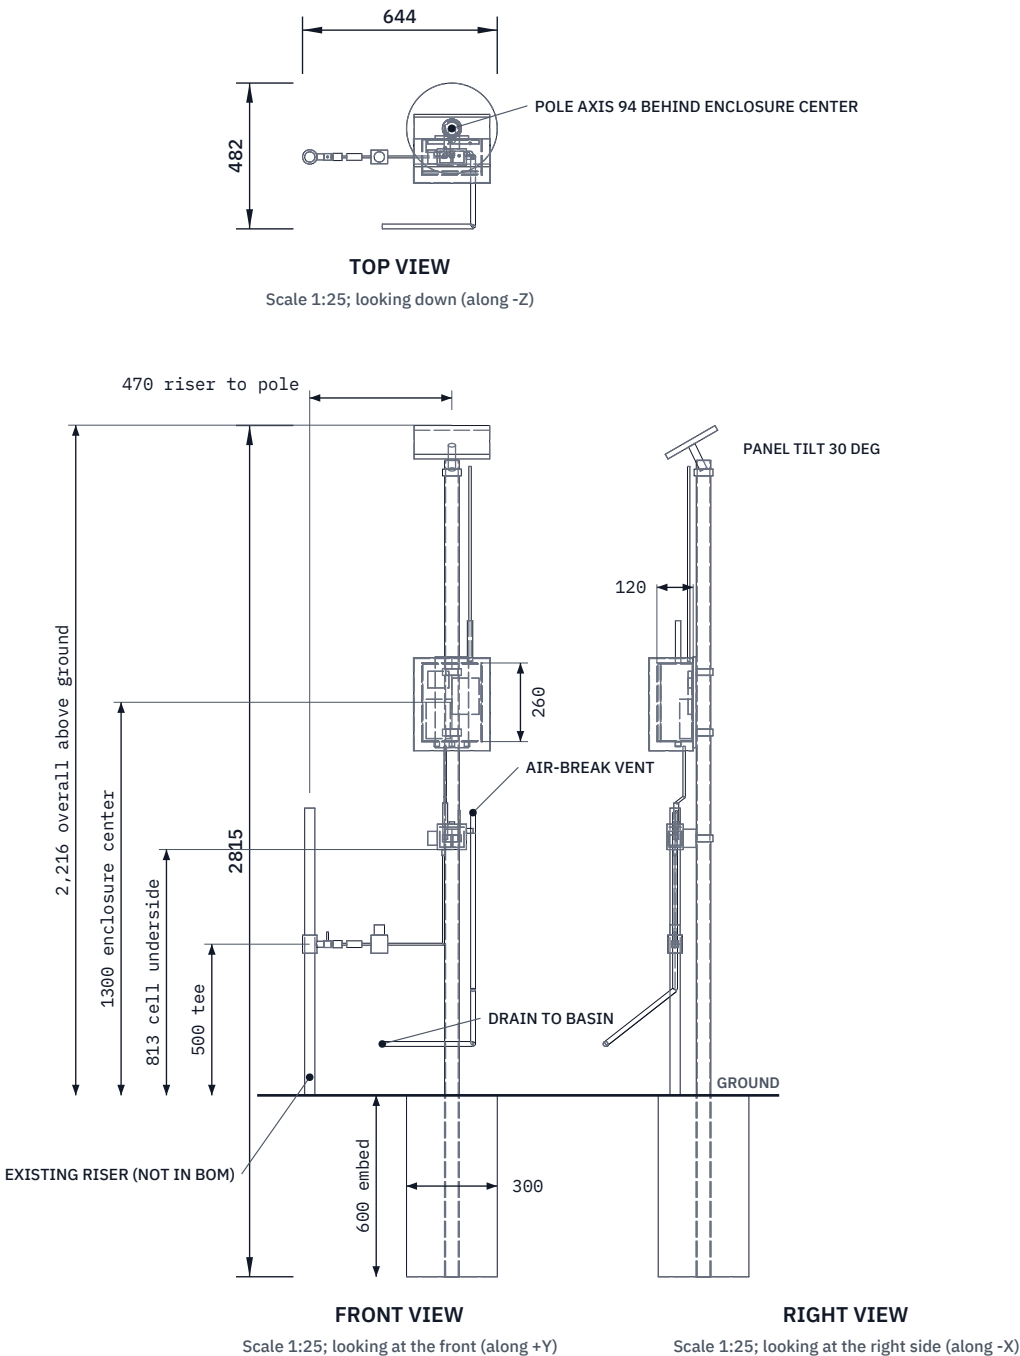

REV	DESCRIPTION	DATE	BY
P1	Preliminary GA for TRL 3 (from cad/src/model.py)	2026-09-25	AC
P2	Plugged pH probe port in cell lid (DDR-002)	2026-09-25	AC
P3	Layout and labels tidied	2026-09-25	AC

MAIN DIMENSIONS AND INTERFACES (MM)

Pole 48.3 x 3.2 galvanized, 2100 above ground, 600 in a 300 footing
Panel 5 W, 250 x 190, tilt 30 deg; top 2,216 above ground
Enclosure IP66 200 x 120 x 260, center 1300; sun shield, 25 gap
Flow cell body 96 x 54 x 74 + 10 lid; cavity 80 x 38 x 66
Cell water 0.19 L; inlet at the bottom, outlet 62 above the underside
Spare 12 pH probe port in cell lid, plugged (DDR-002)
Tee on the 25 mm riser at 500; 1/4 in tube, 738 run, 11 mL
Flush 0.5 L/min (pressure compensating) for 90 s hourly (WWT-CAL-001)
Drain 12 mm bore with open air break; discharges to the basin
Third-angle; front view from -Y, panel and enclosure face toward the equator; riser on the Z axis

WATERWATCH

github.com/BoujeeEnjinia1701/waterwatch

General arrangement

DRAWING NO. WWT - DWG - 001			REV P3	SHEET 1 of 1	SIZE ANSI B
SCALE 1:25	UNITS mm	PROJECTION 	DATE 2026-09-25		DRAWN Amish Chadha
MATERIAL / NOTES Galvanized steel pole; bought-in parts per bom/bom.csv. PRELIMINARY, NOT FOR FABRICATION					
Licensed CERN-OHL-S-2.0 · Design Molecule Lab · designmolecule.com			Generated from cad/src; do not edit by hand		